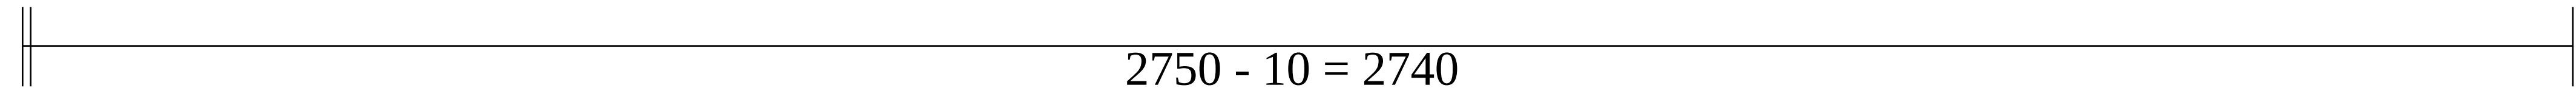


© by Lepton Sistemas

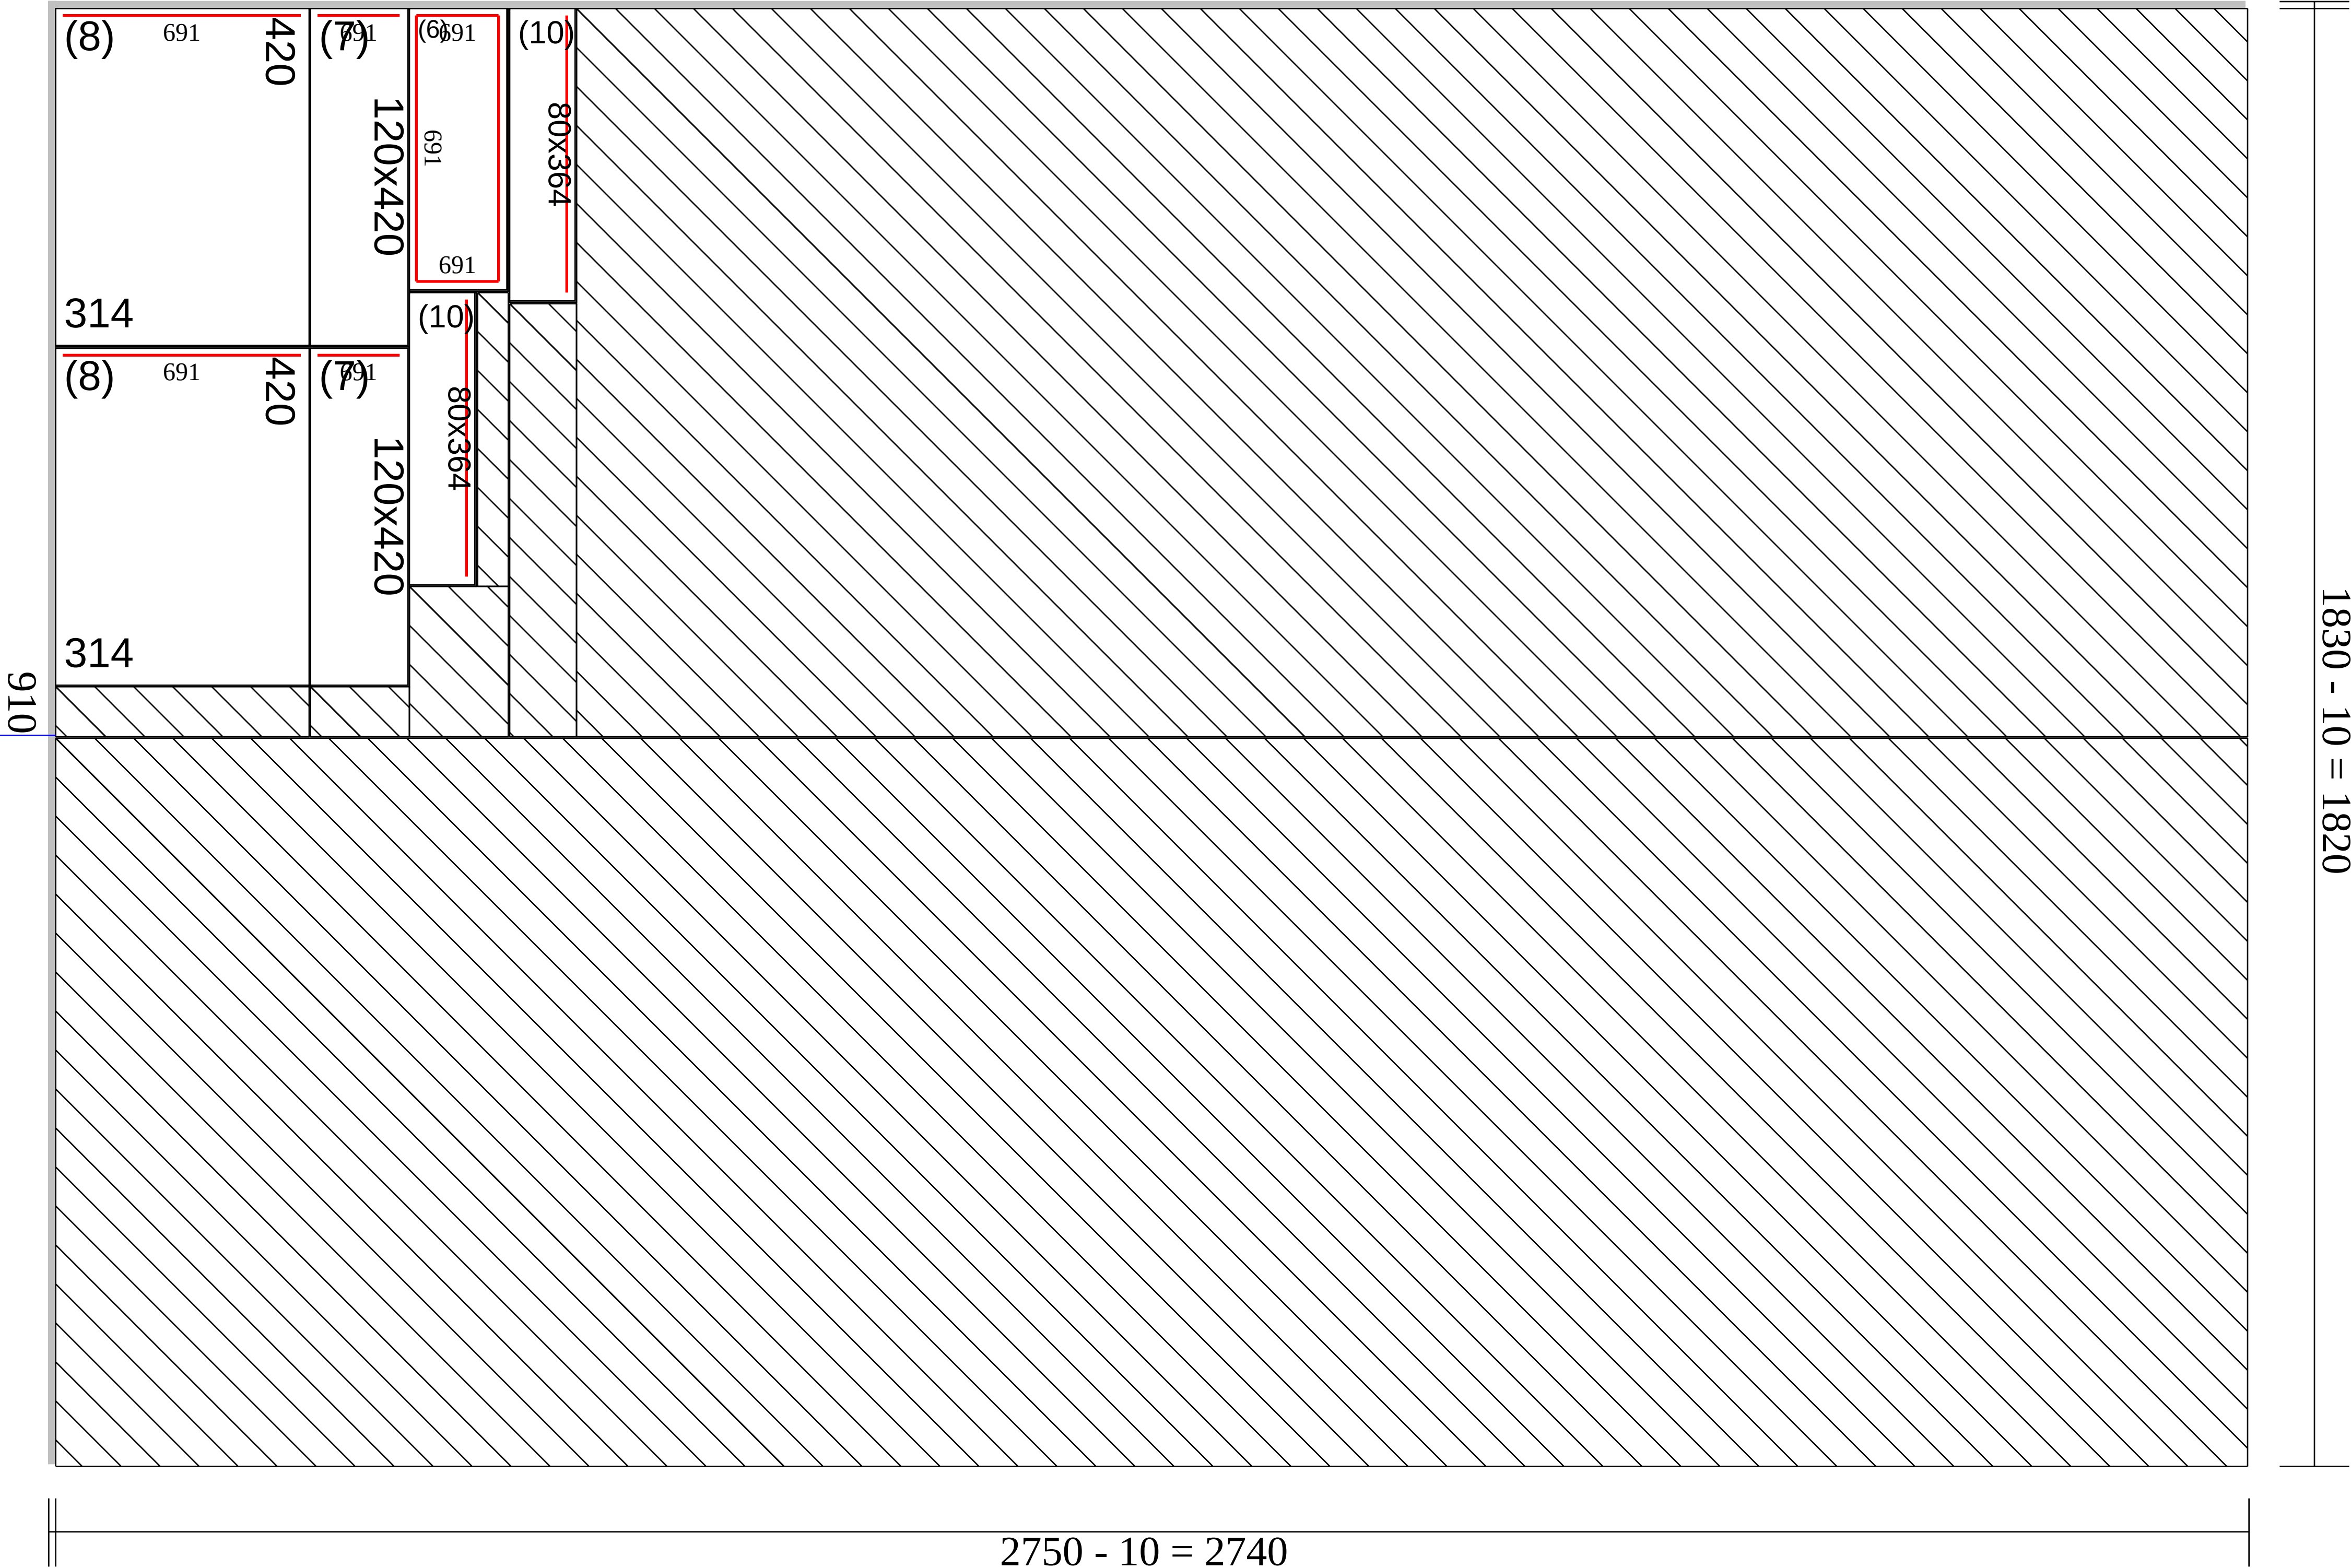


Desplazamientos = 33 por cada placa 22.52 mts

Restos Sobrantes

1 de 2750 x 1830 1/2 Horizontal

© by Lepton Sistemas



Piezas ubicadas

T	Ref.	Cant	Base	Altura	Arr.	Aba.	Izq.	Der.	Detalle
	(8)	2	314	420	691				
	(7)	2	120	420	691				
	(6)	1	120	350	691	691	691	691	
	(10)	2	364	80	691				

Desperdicio = 90.679 % m2 totales = 4.99 m2 Desp = 4.52 m2 Stes = 0.00 m2 cortados= 0.46

Desplazamientos = 13 por cada placa 7.98 mts

 CANTO PVC 22MM BLANCO NATURE x 0.45mm

Restos Sobrantes

Material: MDF FAPLAC BLANCO 18MM. NATURE (Con vetas - 18 mm)

Desperdicio de la sierra: 4.5 mm

Cliente: ARQUIMAX MOSTRADOR RESISTENCIA

Total m2 = 10.1 Cortados = 4.6 Sobrantes 0.0

% de aprovechamiento : 45.250

Refilado x=-10 mm ; y=-10 mm

Cantidad de desplazamientos de la sierra = 46 metros = 30.50

Total de mts lineales: 45.456

CANTO PVC 22MM BLANCO NATURE x 0.45mm

Ml de tapacantos: 17 ml

Pegado de tapacantos: 17 ml

Lados con tapacantos: 32

Cantidad de sobrantes utilizables : 0

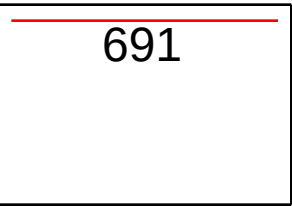
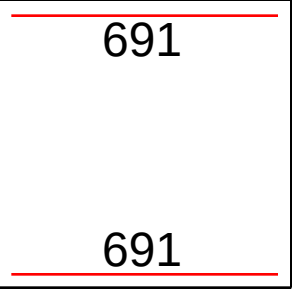
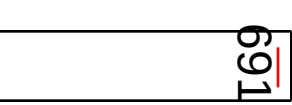
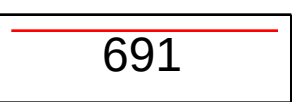
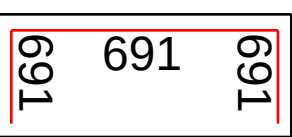
Total m2 sobrantes: 0.000

% m2 utilizables / total m2: 0.000

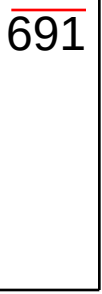
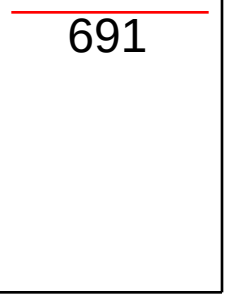
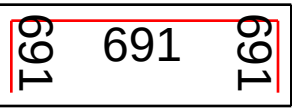
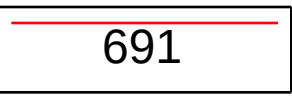
Lista de planchas utilizadas

Cant	Base	Altura	Detalle
1	2750	1830	Placa Entera
1	2740	1820	1/2 Horizontal

Piezas ubicadas

E	Cant	Base	Altura	Observación
	2	717	464	
	2	717	700	
	2	717	114	
	1	1100	250	
	1	1400	500	

E	Cant	Base	Altura	Observación
---	------	------	--------	-------------

	1	120	350	
	2	120	420	
	2	314	420	
	2	287	80	
	2	364	80	
	1	300	1800	
	12	290	200	

Total de piezas cortadas: 30 Total m2: 4.6 Total ml: 45.5

 CANTO PVC 22MM BLANCO NATURE x 0.45mm=17.2ml